SAPHYRE Spatial Database

First Floor

Kirkland House

10 0 10 20 30 40 Feet

- General Use
- Instructional
- Offices
- Residential
- Special Use
- Support

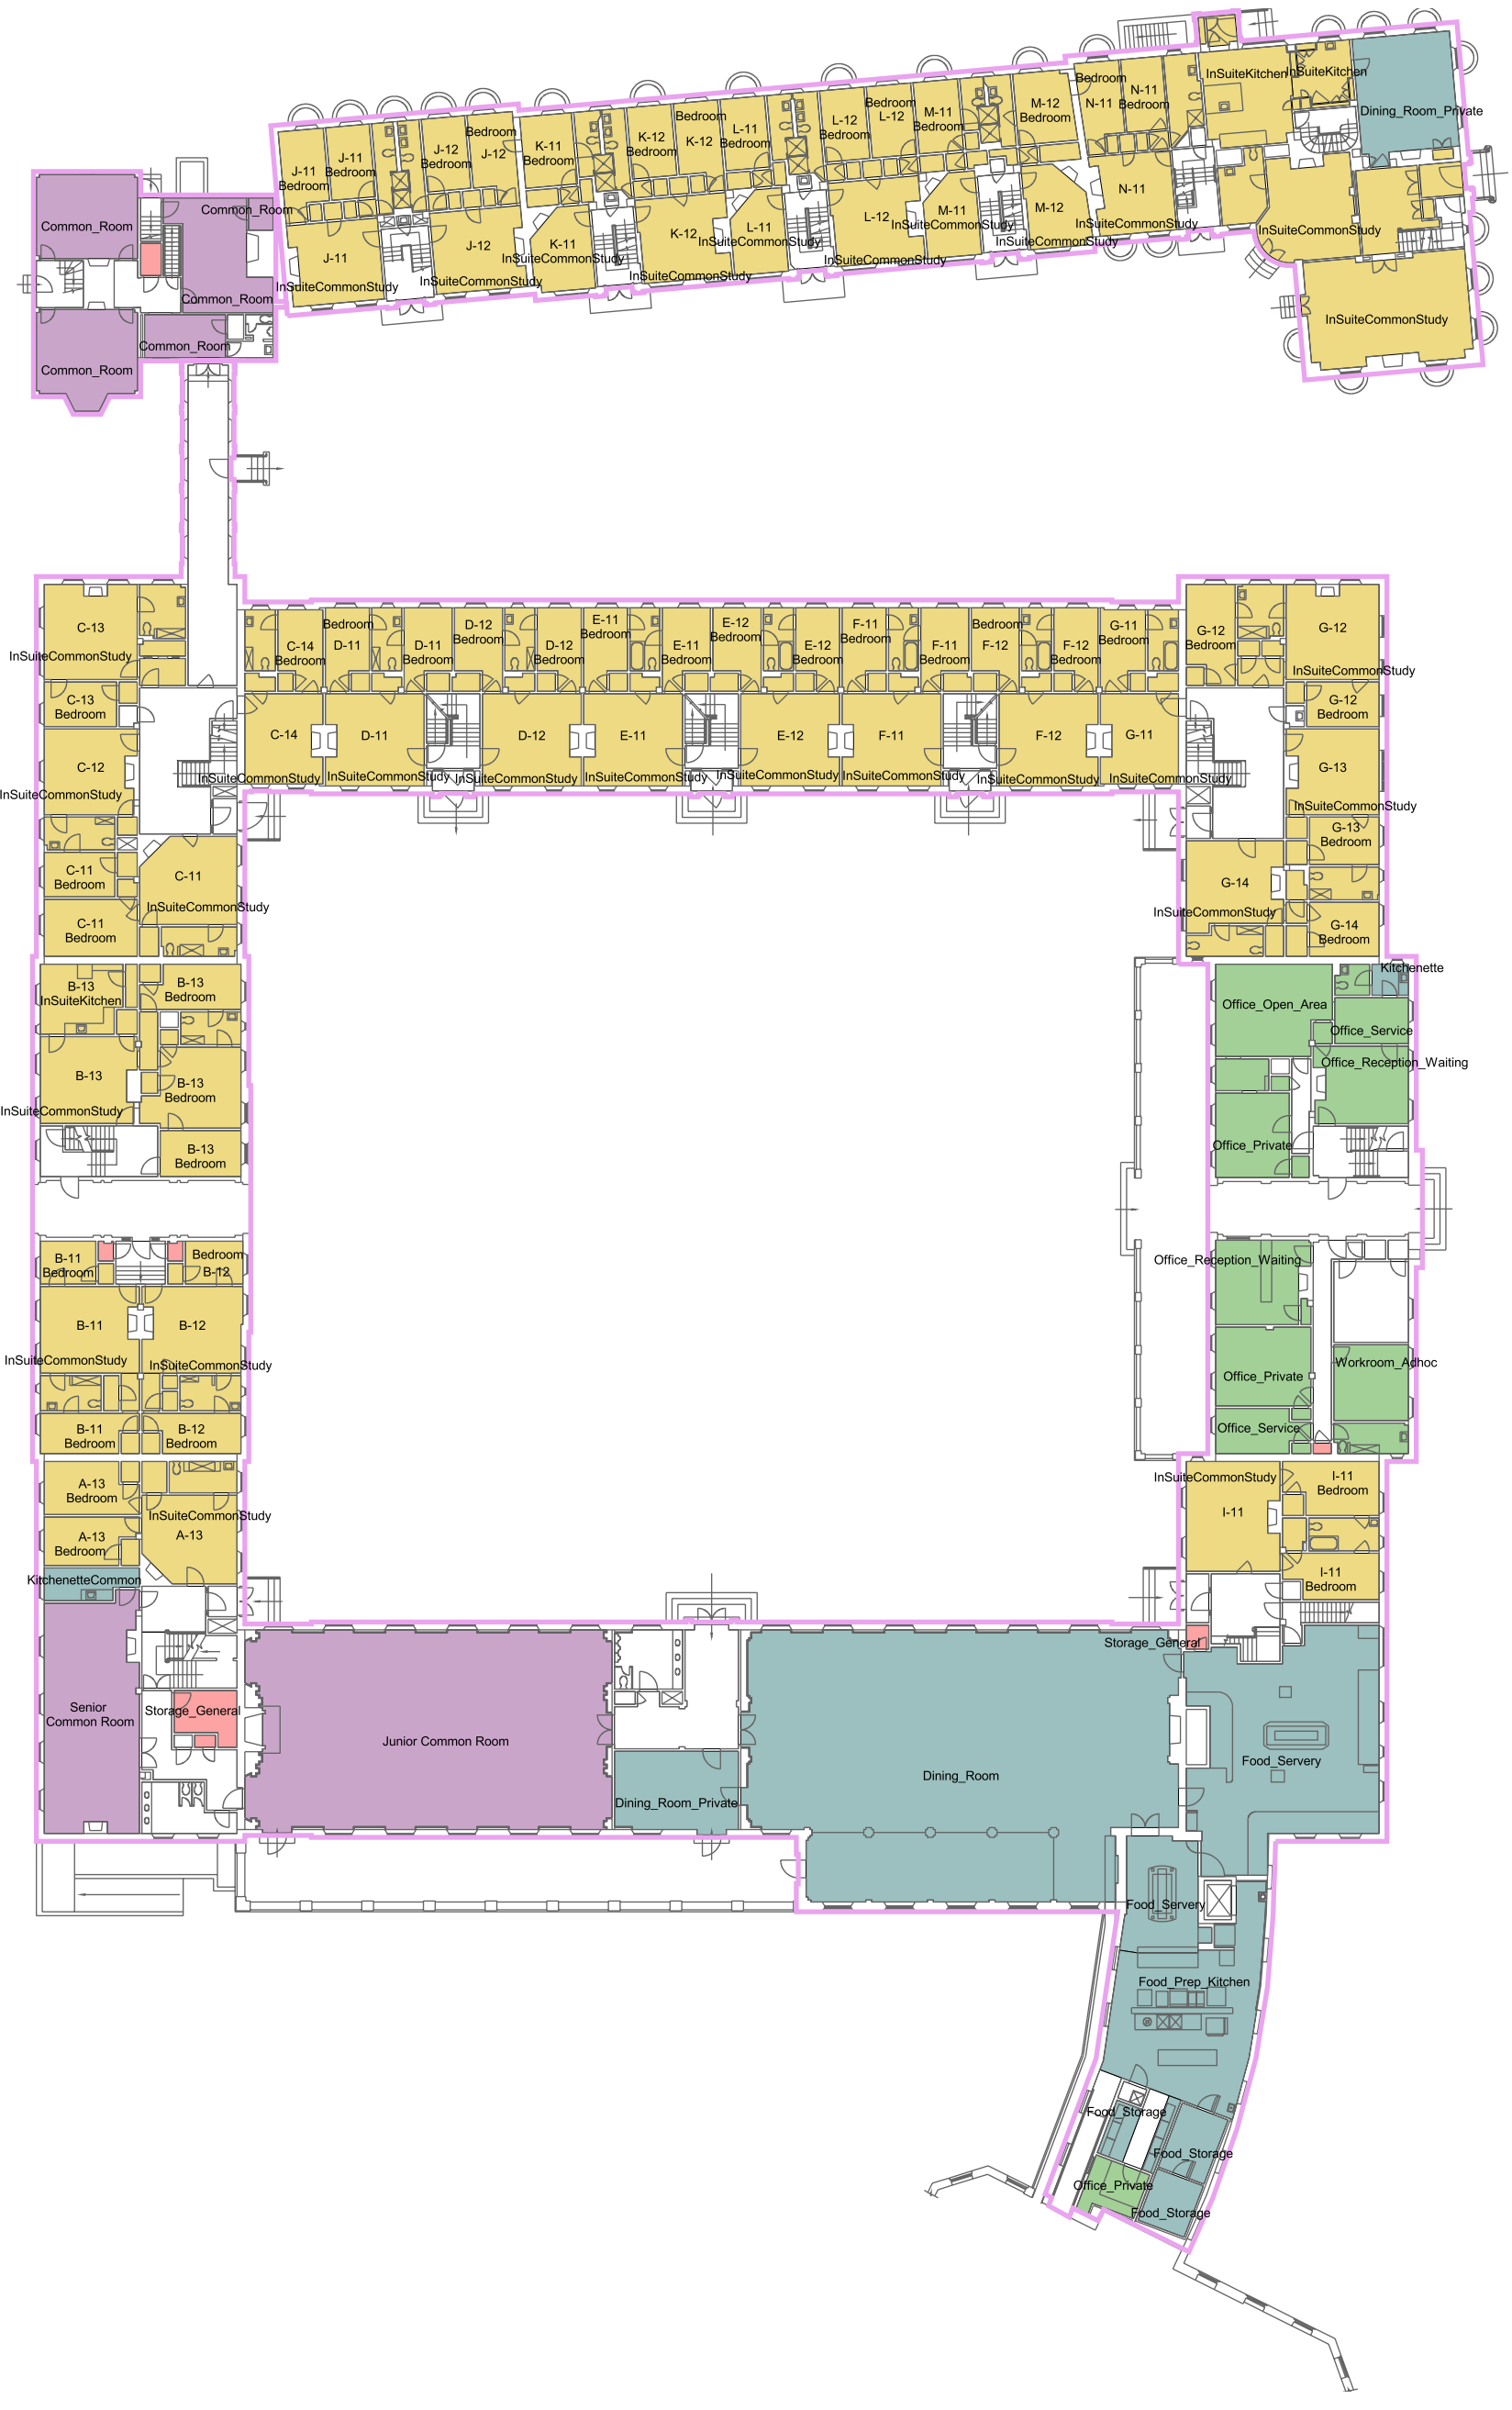

SAPHYRE Spatial Database

Second Floor
Kirkland House

10 0 10 20 30 40 Feet

- General Use
- Instructional
- Offices
- Residential
- Special Use
- Support

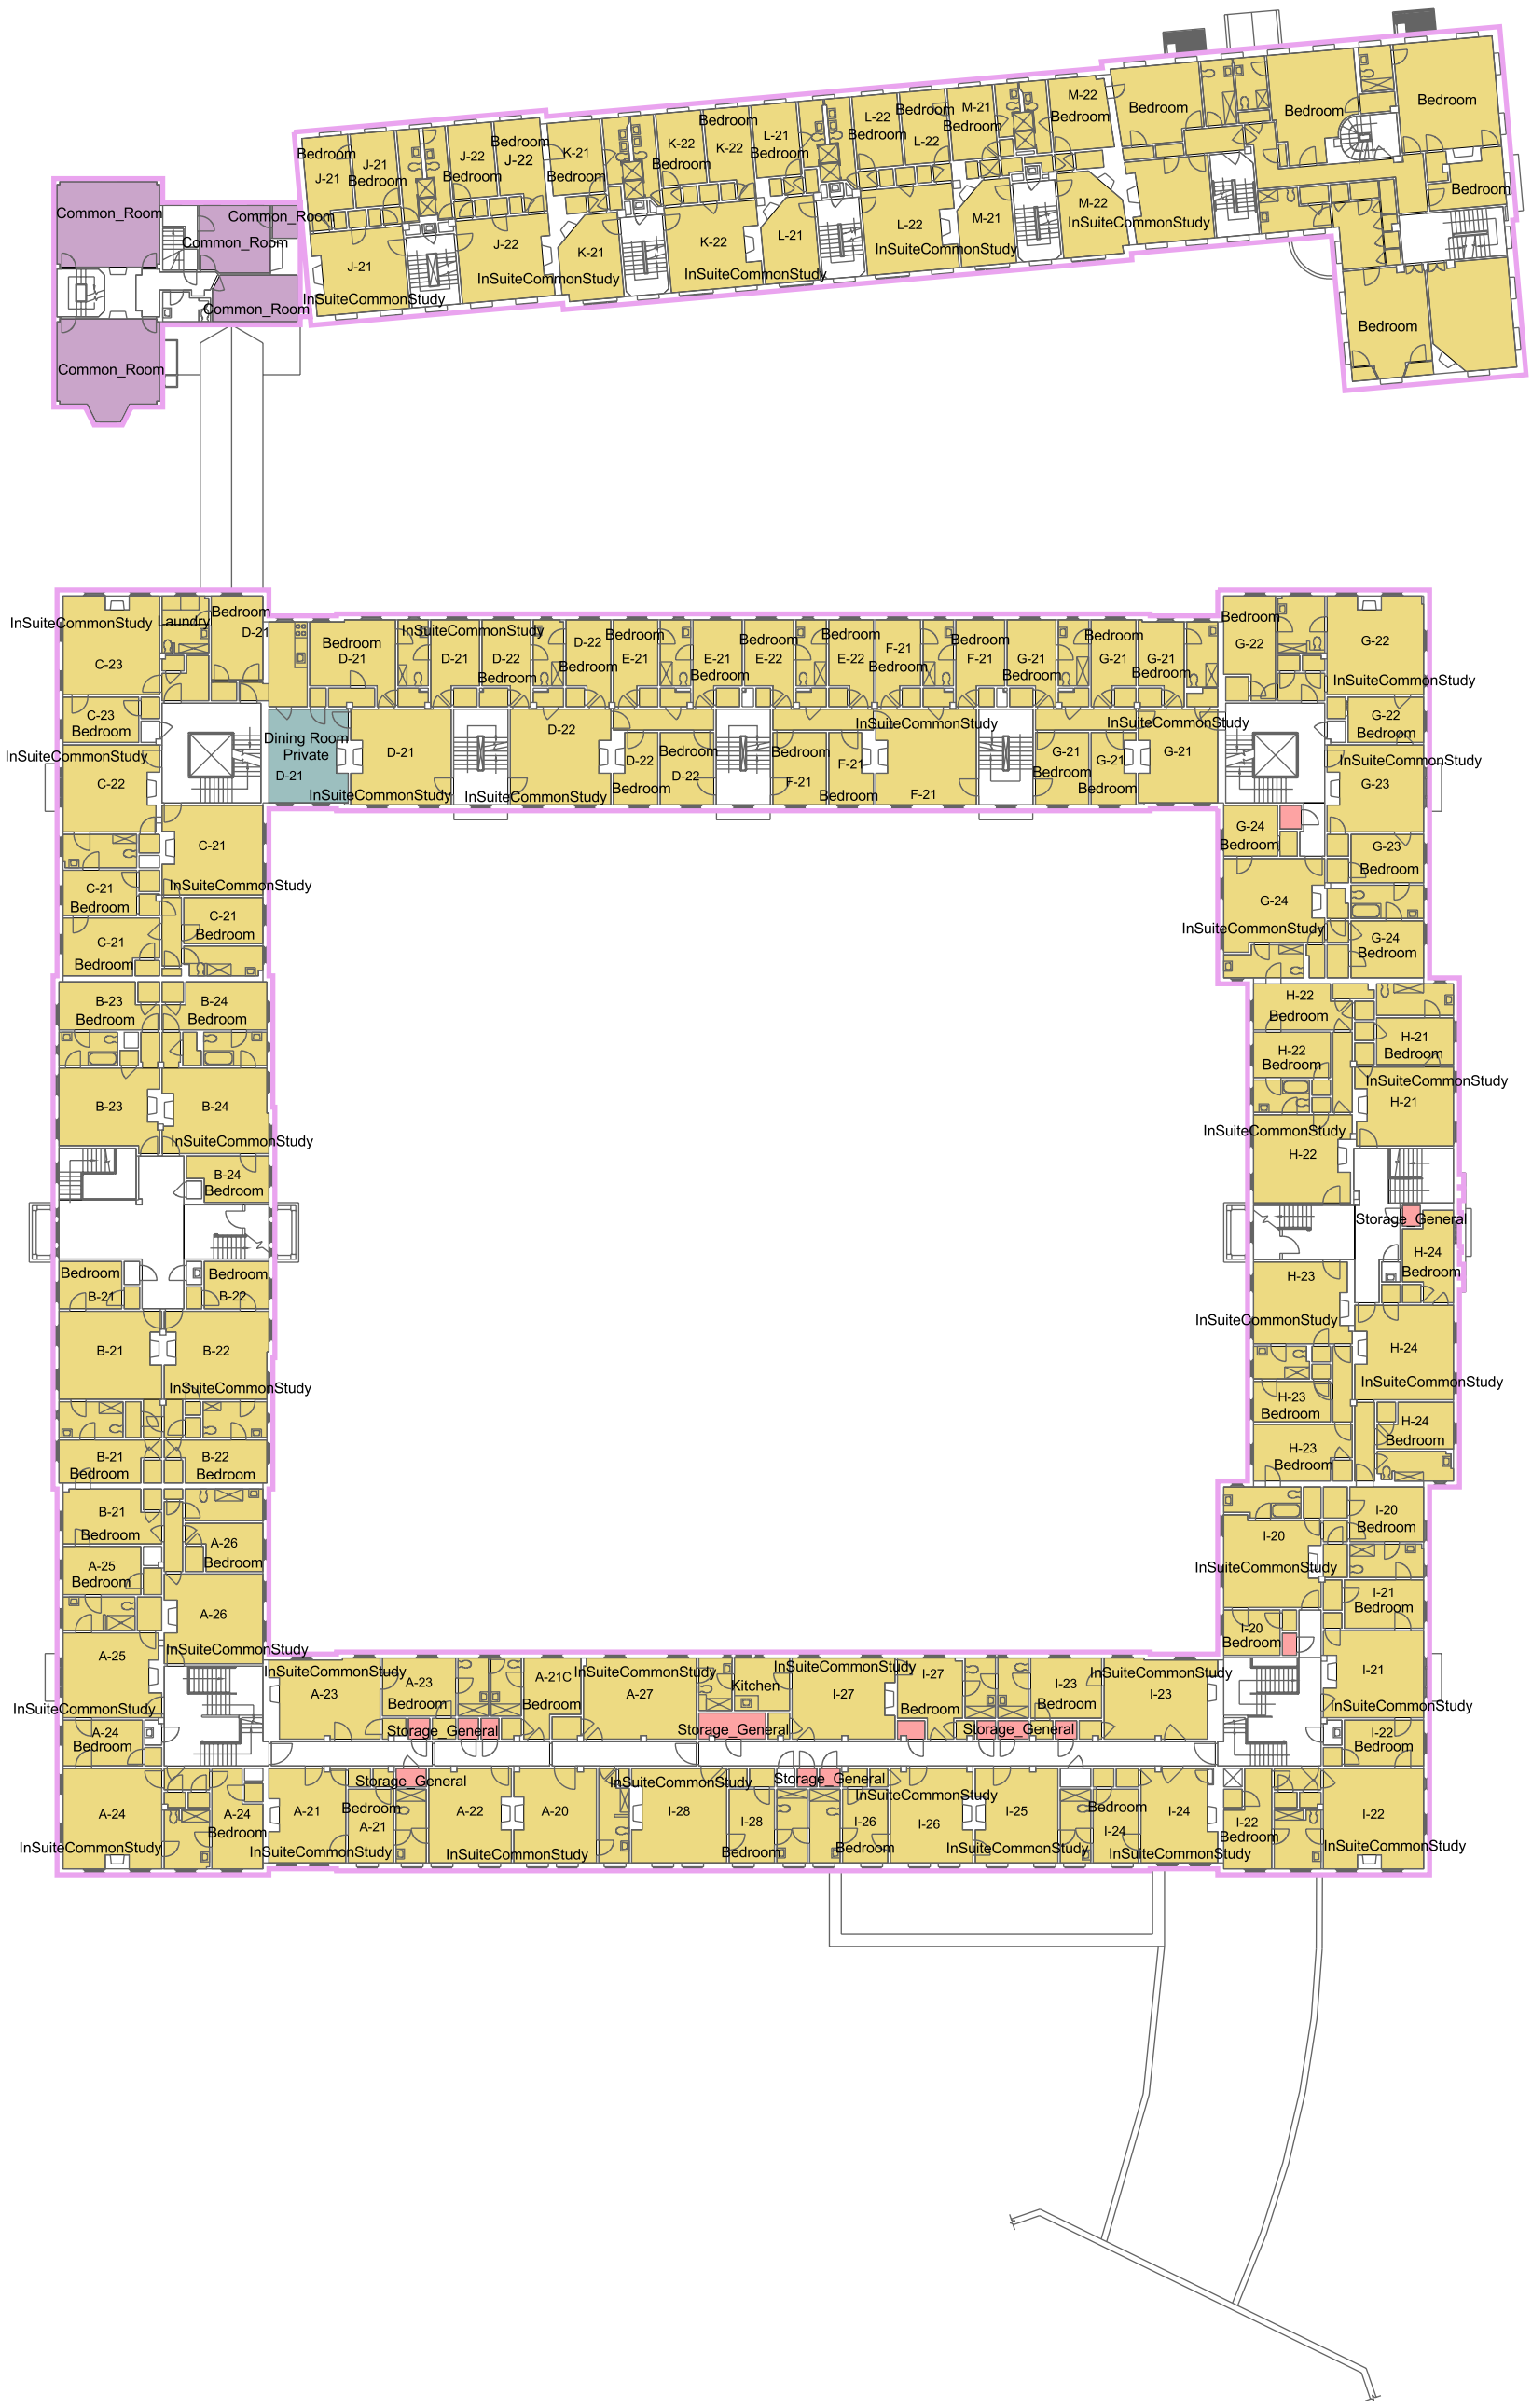

SAPHYRE Spatial Database

Third Floor

Kirkland House

10 0 10 20 30 Feet

- General Use
- Instructional
- Offices
- Residential
- Special Use
- Support

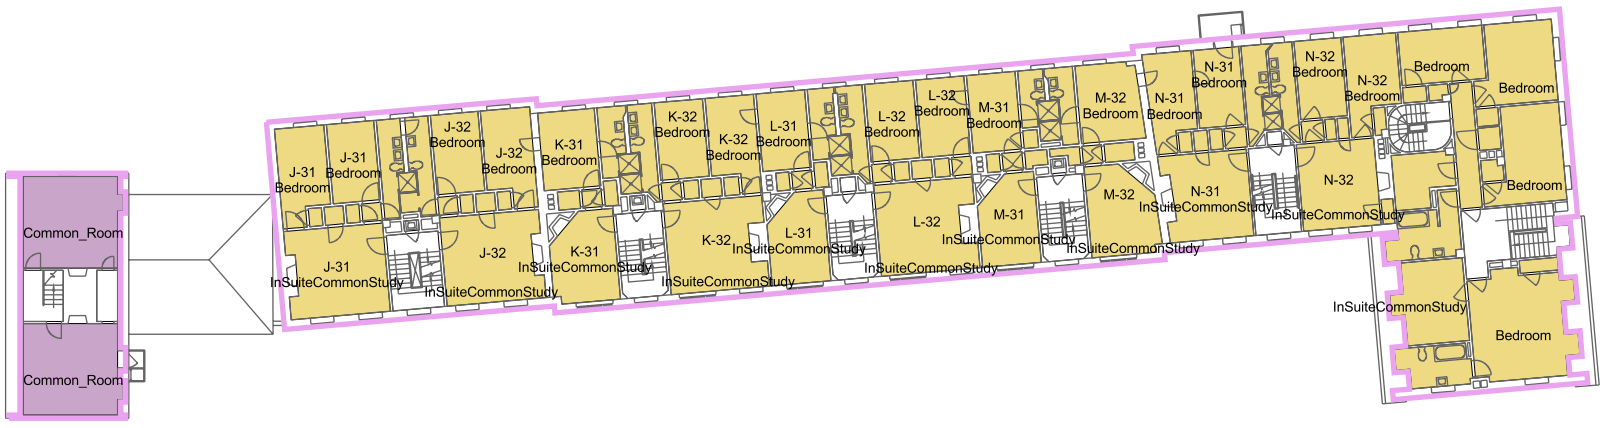

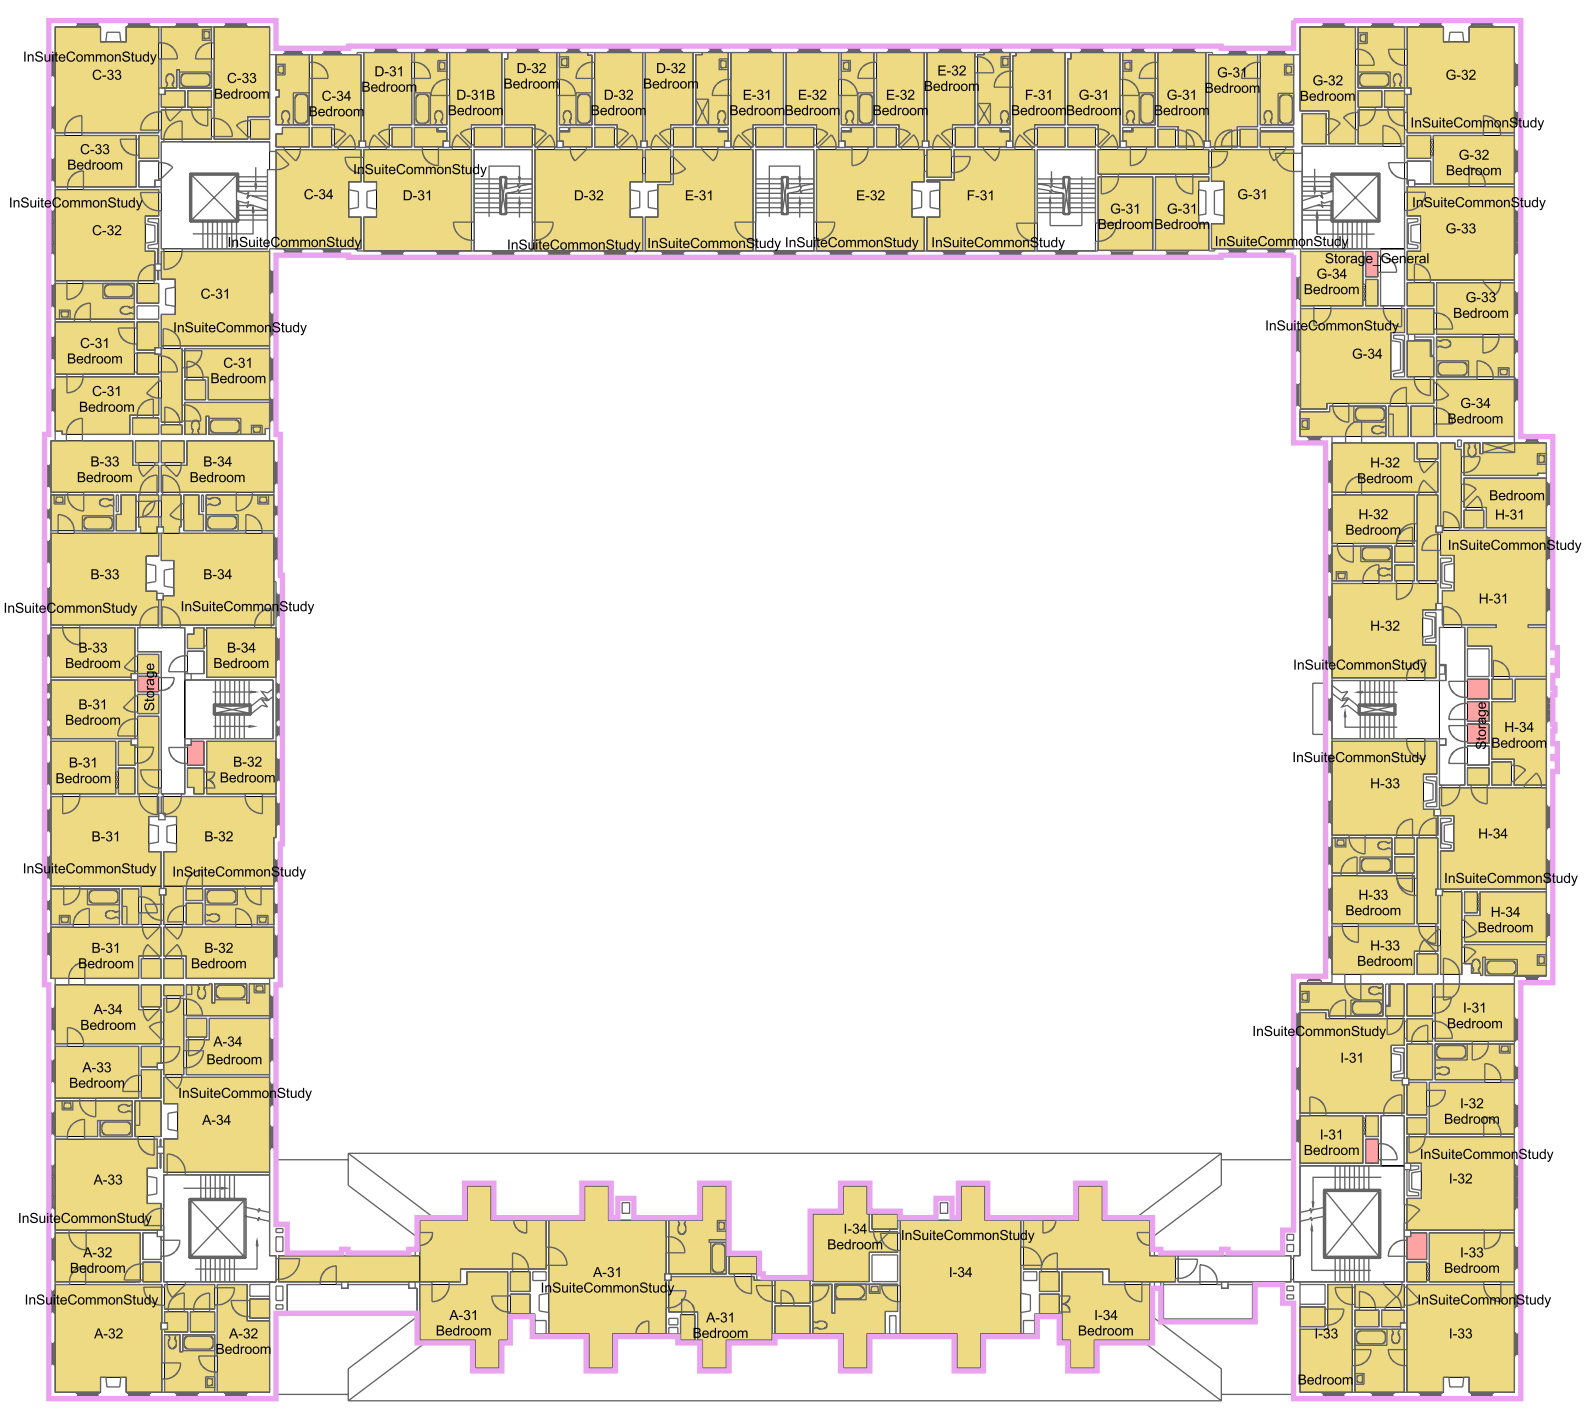

SAPHYRE Spatial Database

Fourth Floor

Kirkland House

10 0 10 20 30 40 Feet

- General Use
- Instructional
- Offices
- Residential
- Special Use
- Support

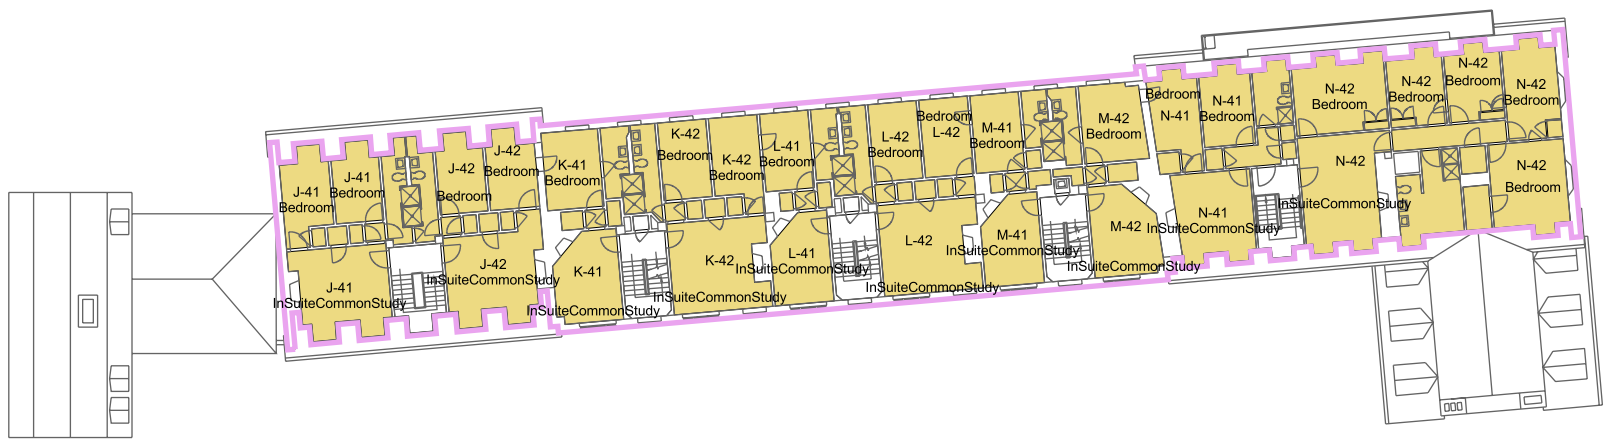

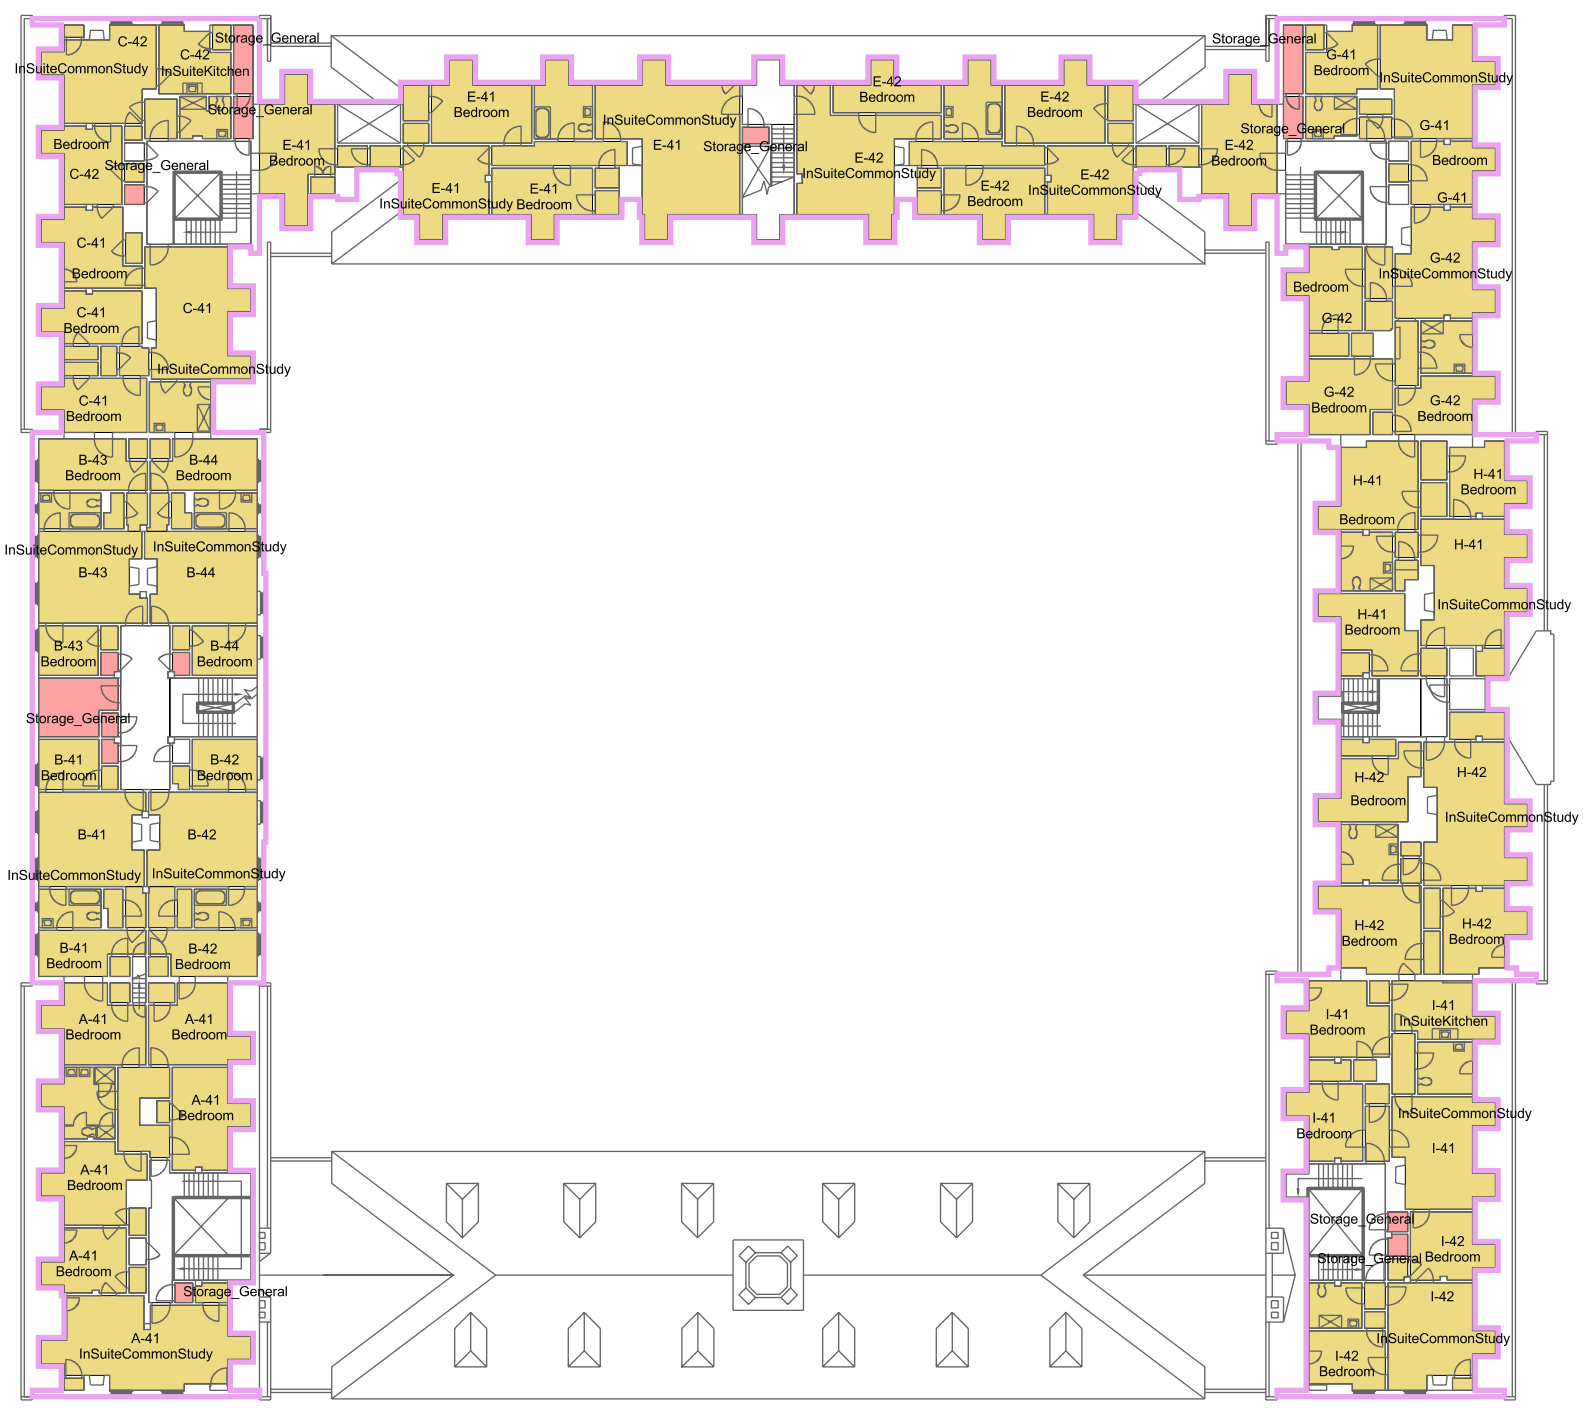

SAPHYRE Spatial Database

Fifth Floor

Kirkland House

10 0 10 20 30 40 Feet
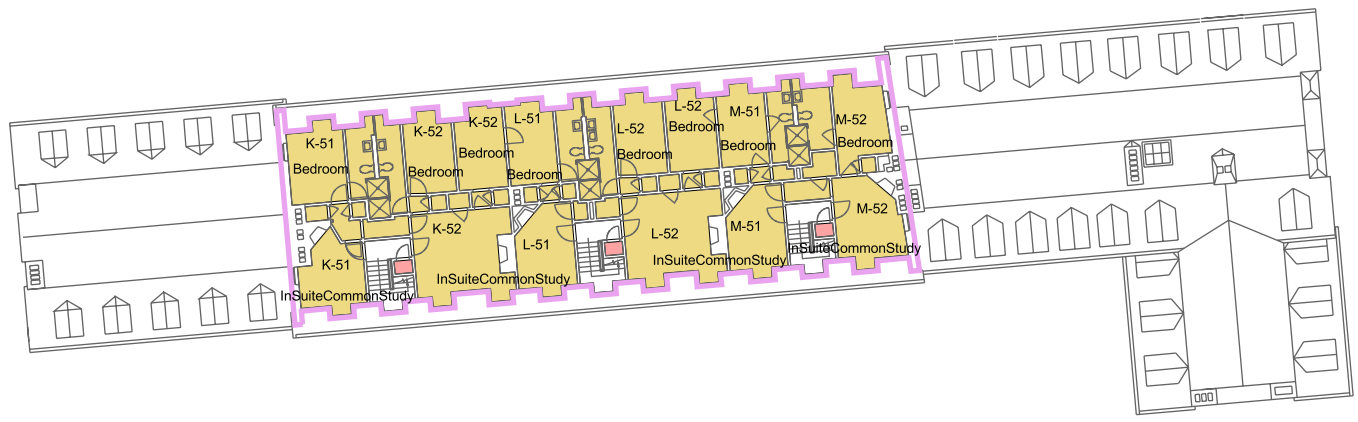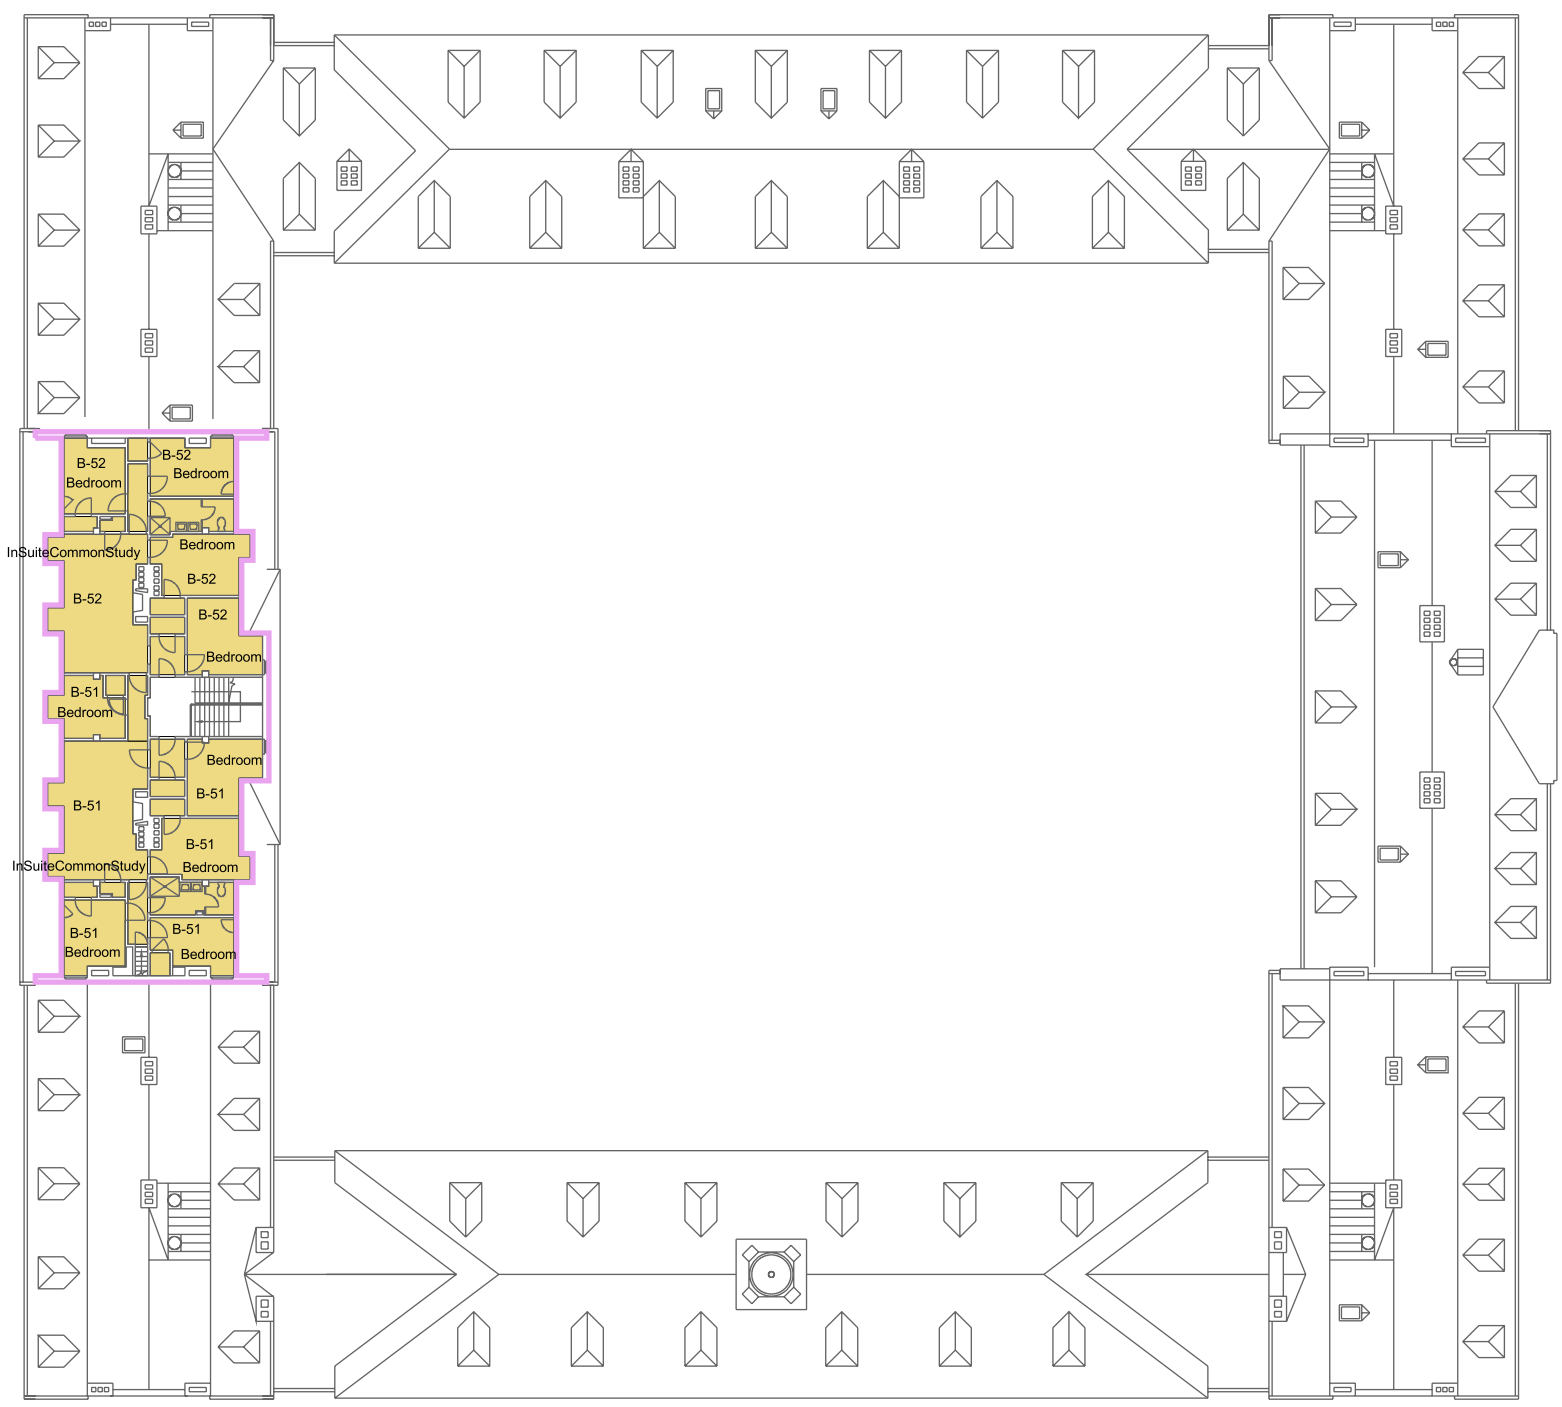
- General Use
- Instructional
- Offices
- Residential
- Special Use
- Support